HOMEKONCEPT 102 G2 · DZIAŁKA 750/73

Dom dosunięty do drogi · garaż i taras na dole · skala 1:250

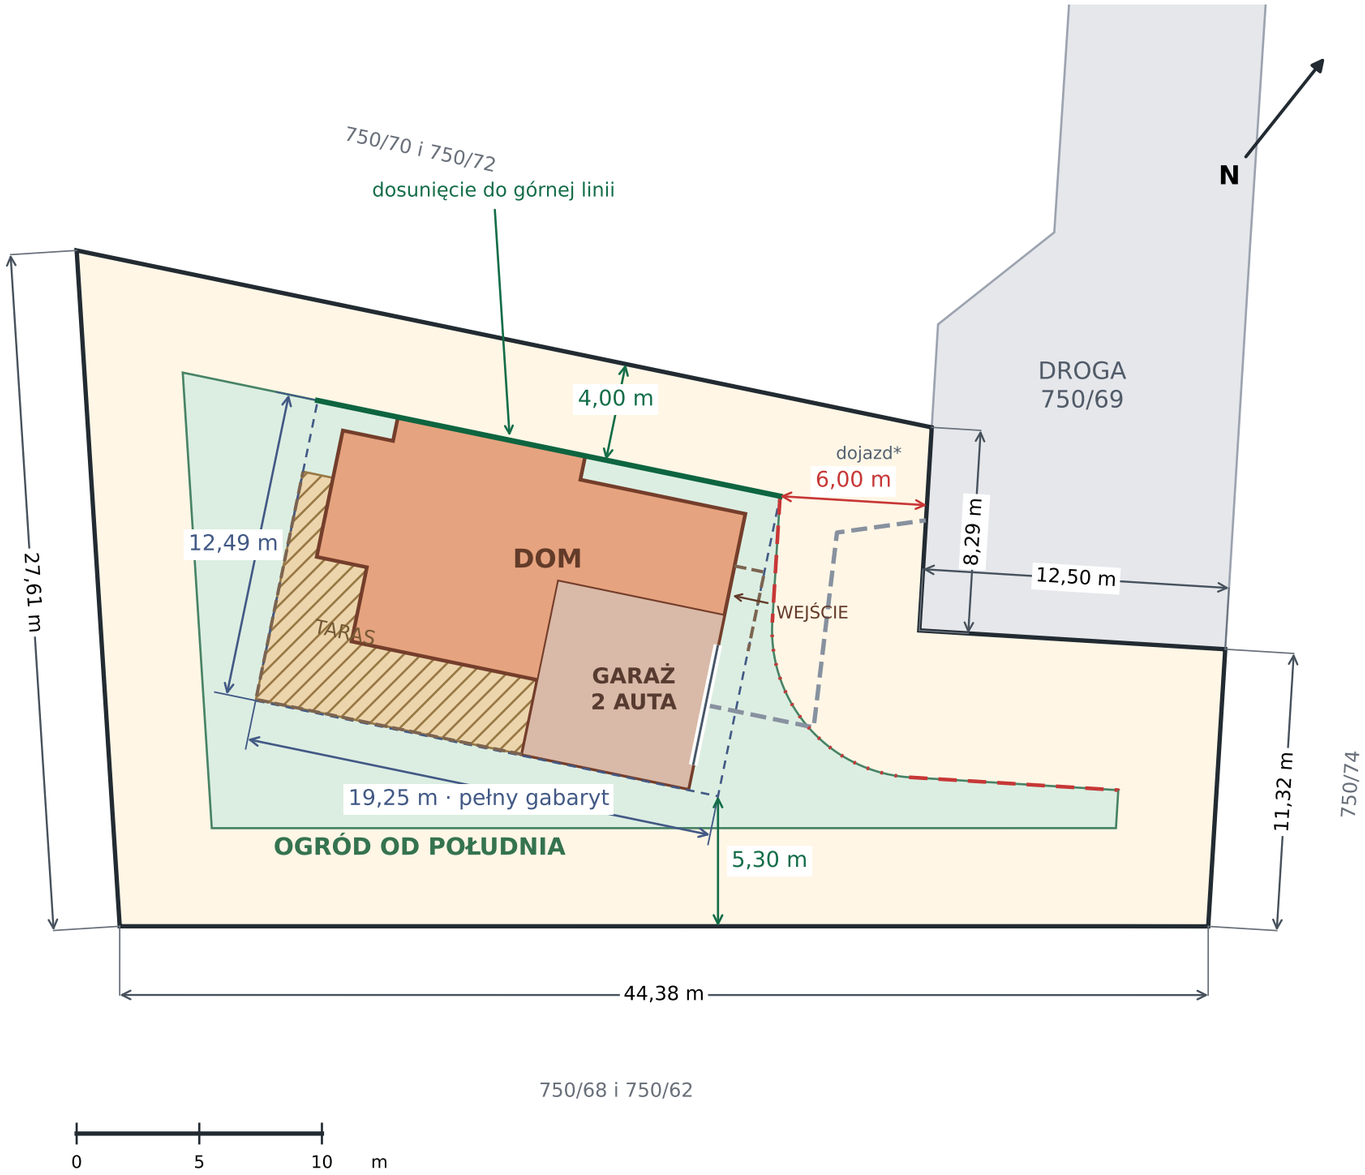

MIEŚCI SIĘ GEOMETRYCZNIE

Przesunięcie ku drodze: 2,19 m,
Cały gabaryt 19,25 × 12,49 m mieści się w obszarze po odsunięciach,
Górna krawędź nadal na zielonej linii,

POWIERZCHNIA ZABUDOWY

165,87 m²

17,57% powierzchni działki
Limit 20%: 188,80 m²
Zapas: 22,93 m²

ODLEGŁOŚCI PEŁNEGO GABARYTU

Od górnej granicy działki: 4,00 m
Od drogi: min, 6,00 m
Od dolnej granicy: min, 5,30 m

Odległości liczone do całego gabarytu, więc obejmują również taras i detale.

UKŁAD

Zachowano kąt i odbicie projektu.
Dom przesunięty wzdłuż górnej linii do styku z granicą 6 m od drogi.
* Trasa dojazdu to schemat, bez weryfikacji manewrów pojazdów.

Pomarańczowy: obrys ścian Brązowy: garaż Szraf: taras Niebieska ramka: pełny gabaryt Czerwona linia: 6 m od drogi

Obrys odtworzony z rysunku wymiarowego HOMEKONCEPT; rysunek analityczny, nie projekt zagospodarowania terenu.

6 m przyjęto od obu odcinków styku z drogą, 4 m od pozostałych granic. Pełnej WZ nie udostępniono. Płaski dach garażu wymaga sprawdzenia w WZ.

Źródła: ULDK 26.10.2026; HOMEKONCEPT 102 G2, rzut parteru i dane techniczne. Powierzchnia 165,87 m² to wartość katalogowa, nie pole szkicu.

Obliczenia w EPSG:2177. Sytuowanie geometrii, prawa do drogi, sieci, ppoż. oraz pozostałe parametry WZ wymagają weryfikacji przez architekta.

A3 · 1:250 · 26.10.2026